Propriété dite : Casa Anfa 132

Située à :Casablanca,Préfecture et Arrondissement Hay Hassani,Projet Casa Anfa.

Titre : 22695/64

PLAN TOPOGRAPHIQUE DE COPROPRIETE

Légende :
- Limite de la Partie Privative
- Limite de la propriete
- Partie commune
- Murs ,Piliers et Gaines

Echelle 1/100

Plan Produit par le requérant

NORD الشمال

PLAN DU REZ DE CHAUSSEE IMMEUBLE G+H

Des cotes 0.00m et 1.85m à la cote 5.30m.

Echelle des Hauteurs au 1/200
Suivant la coupe A – B

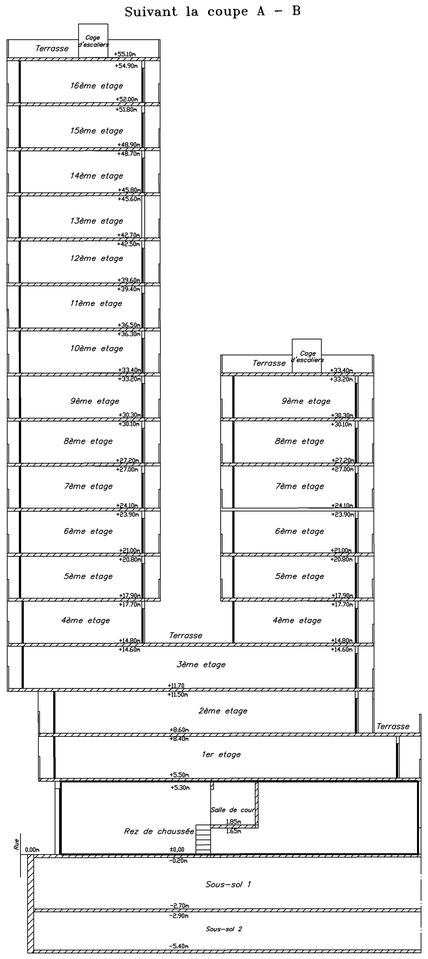

Boulevard de l'Aéropostale (Tramway) de 41m T.22696/64

Immeuble A+B

Tableau des contenances

جدول المساحات

Propriété dite	Titre	Indices des parties		situation	Surface (m^2)		Consistances	Observations
		Privatives	Communes		A l'interieur du titre	Totale avec surplomb		
Walili 188	T.55796/64	203		Rez de chaussée	294	294	Magasin	A laquelle liée la PPN°203A au 1ER Sous sol
Walili 189	T.55797/64	204			438	438	Salle de sport	A laquelle liée la PPN°204A au 1ER Sous sol et la PPN°204B au 2EME Sous sol
Walili 190	T.55798/64	205			190	190	Magasin	A laquelle liée la PPN°205A au 1ER Sous sol Dont 45m² de Jardin
Casa Anfa 132	22695/64		2		170	170	2Cage d'escaliers,4Asc et 2Escaliers de Secour	
			5^A		76	76	Vide sur Rampe	
			3		65	65	Murs,piliers et gaines	
			TOTAL		1233	1233		
			31		3803	3803	Jardin,passage,Entrée et Guérite	
			160		34	34	Poste d'Electricité	
			Imm.A,B,C,D,E etF		3496	3496	Autre immeubles	
			TOTAL		8566	8566		

Plan d'Ensemble
Echelle 1/1000

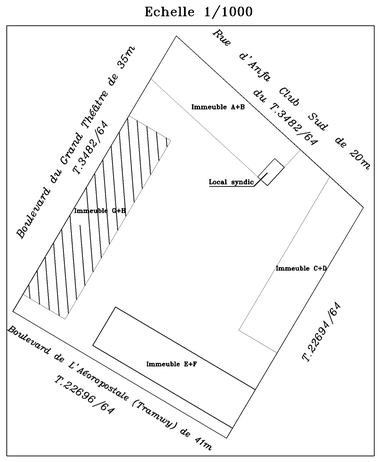

DIRECTION DU CADASTRE

Plan levé par le Géometre:M'hamed AZAIZI
Dessinateur : Naim Chaibia

Plan certifie conforme a l'état des lieux en : Mai 2018

Mappe de reperage au 1/1250-28-17-e-15 A-B/2-3
Carte Topographique au 1/50000 Casablanca

Morcellement du T:3482/64 secteur:1 tranche:1d (Lot:132)

تجزئة رسم : 3482/64 قطعة 132 بقعة : 1 المنطقة : 1

الملك المسمى : كازا أنفا 132
الكائن : بالدار البيضاء عمالة مقاطعة الحي الحسني، مشروع كازا أنفا.
رسم : 64/22695